


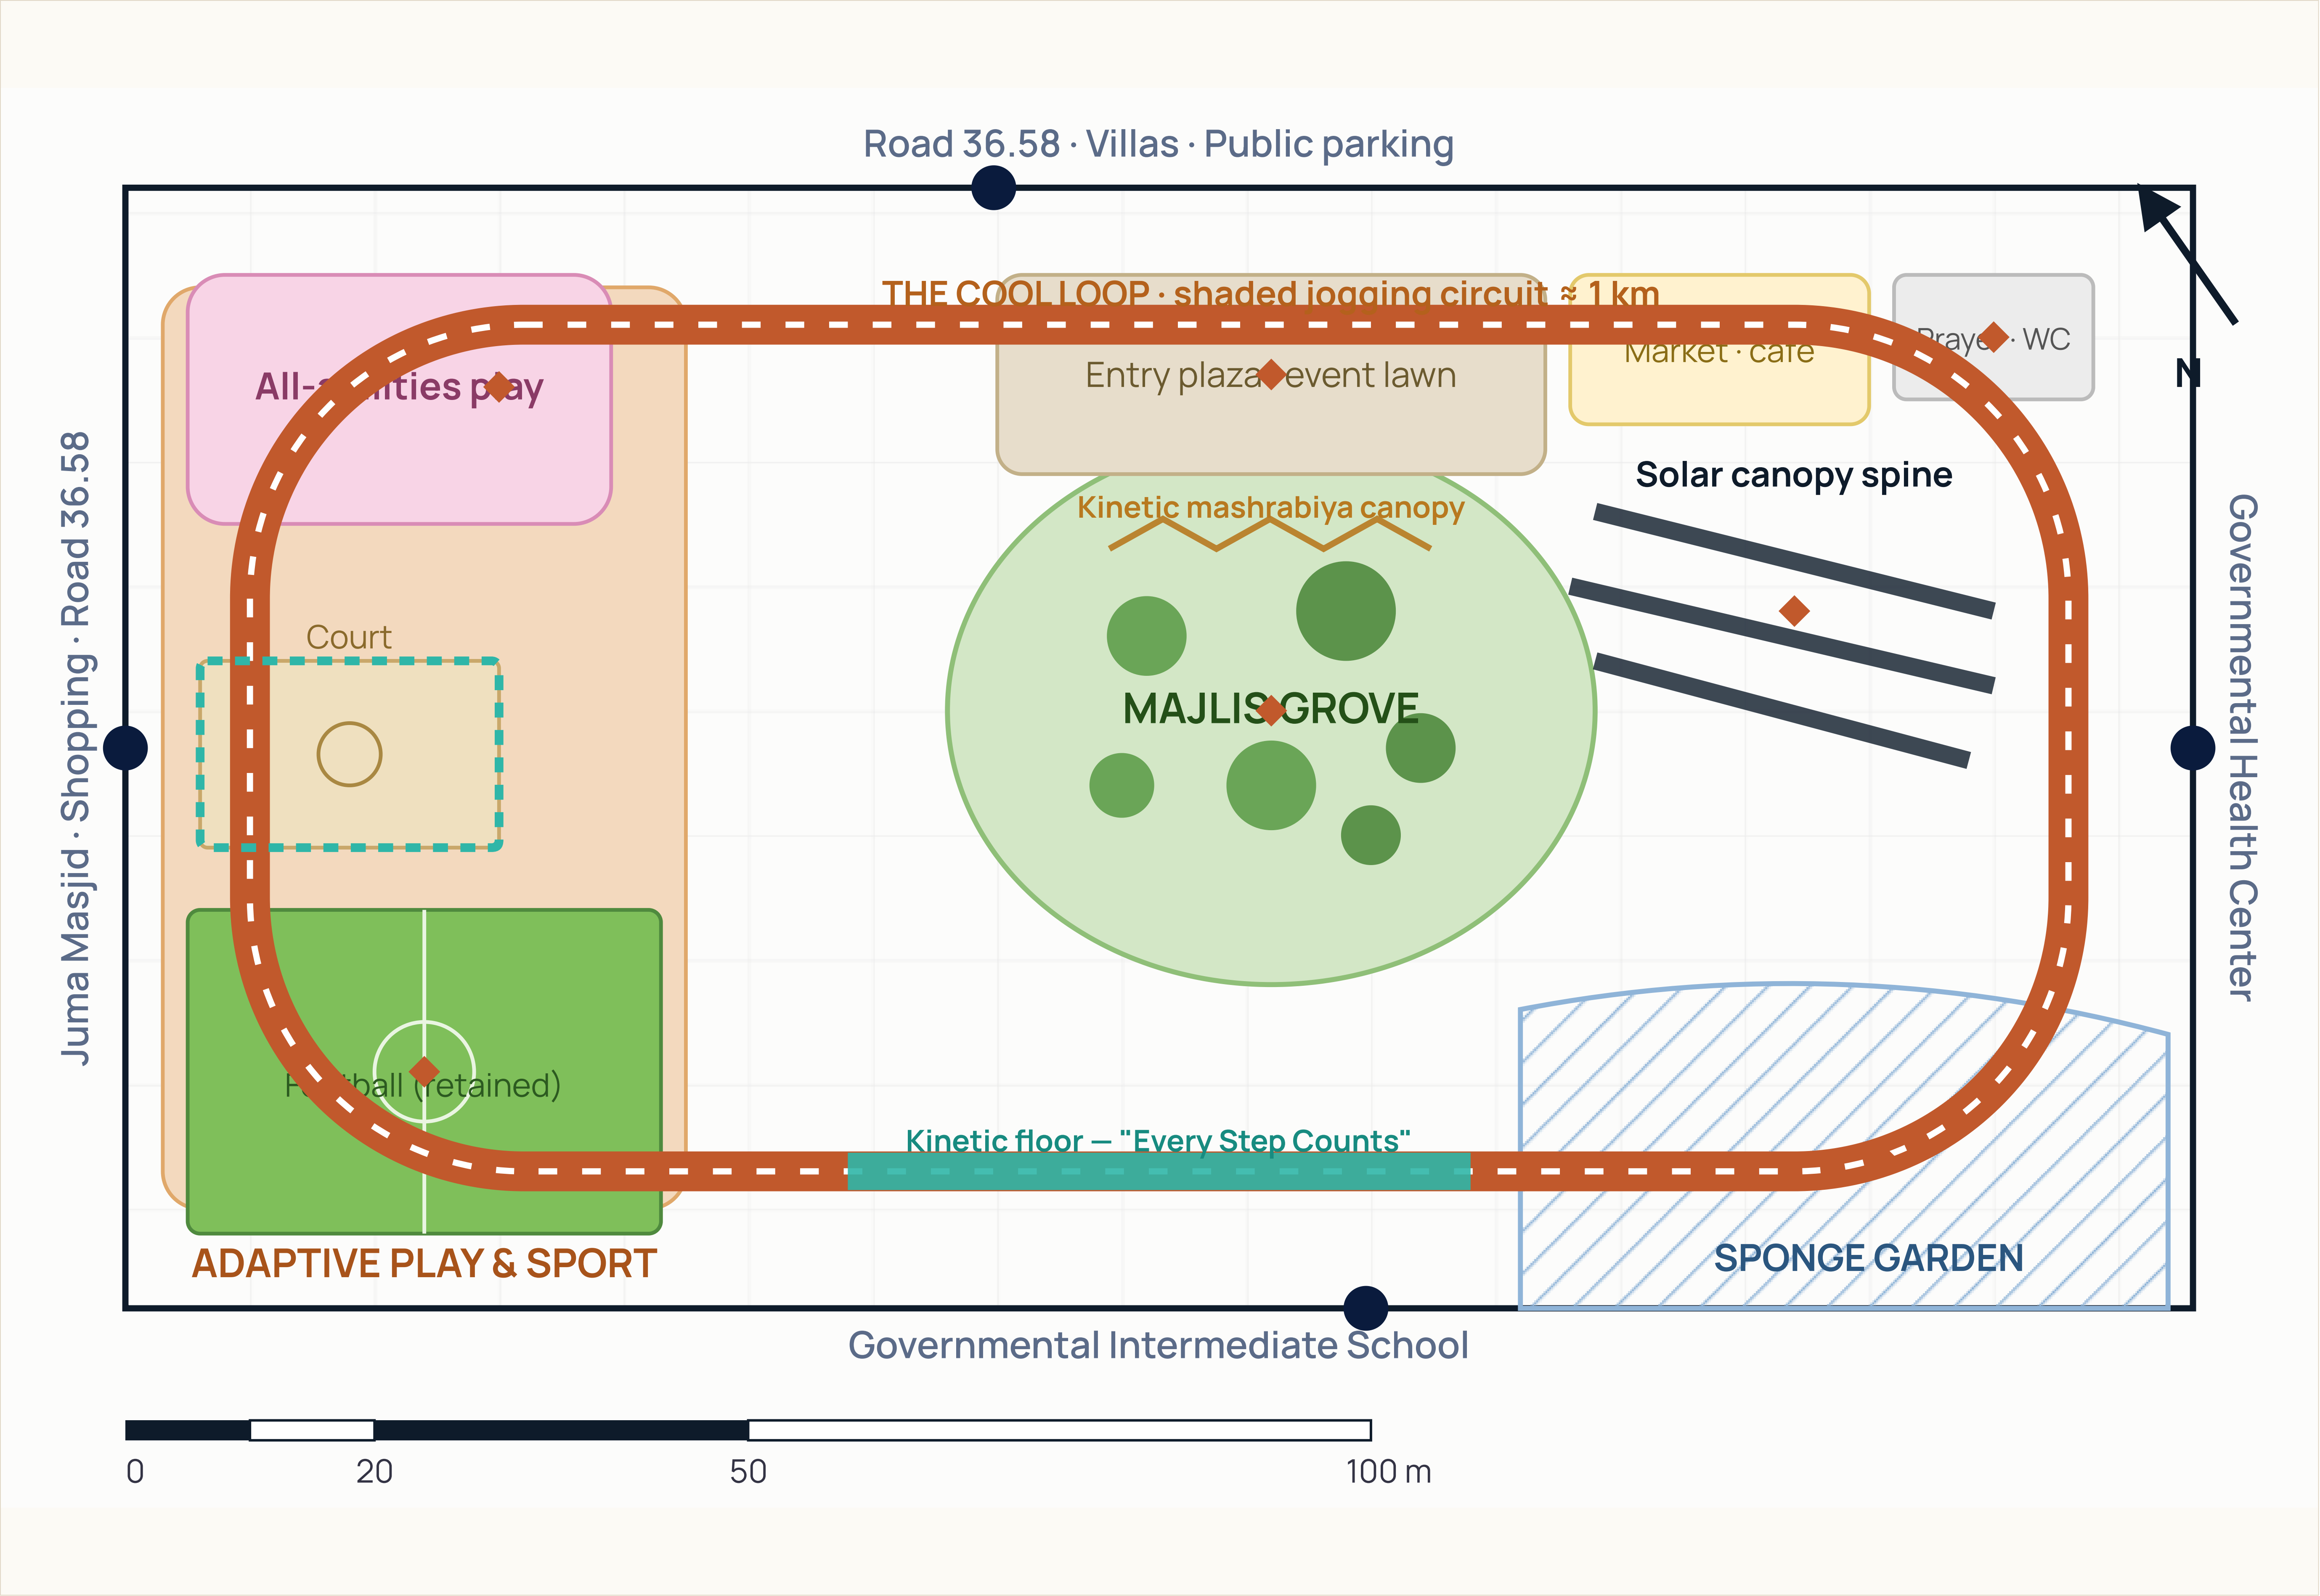

Zones

- Adaptive Play & Sport
- Majlis Grove (social core)
- Sponge Garden (bioswales)
- Market · café · services
- Event lawn / plaza
- Cool Loop – jogging ≈1 km
- Solar canopy spine (PV)
- Identity gateway (x4)
- Comfort Brain sensor node
- “Every Step Counts” kinetic floor
- Kinetic mashrabiya canopy


Programme areas (approx.)

Total site 15,000 m²
Shaded circulation ≈ 3,100 m²
Majlis Grove & plaza ≈ 2,600 m²
Play & sport (retained+new) ≈ 3,000 m²
Sponge Garden & planting ≈ 3,800 m²
Market/café/services ≈ 900 m²
Leasable (commercial) ≈ 15%

Design intent

A shaded Cool Loop wraps the whole park; the quiet Majlis Grove sits in the cool core under a sun-tracking kinetic mashrabiya; sport is retained at the SW end; the Sponge Garden lines the school edge. A network of Comfort Brain sensor nodes and two “Every Step Counts” kinetic-floor zones (court + a Cool-Loop stretch) make the park interactive and self-tuning. One identity gateway addresses each neighbour.

Concept-level to-scale layout. Areas indicative; to be coordinated with survey & services.

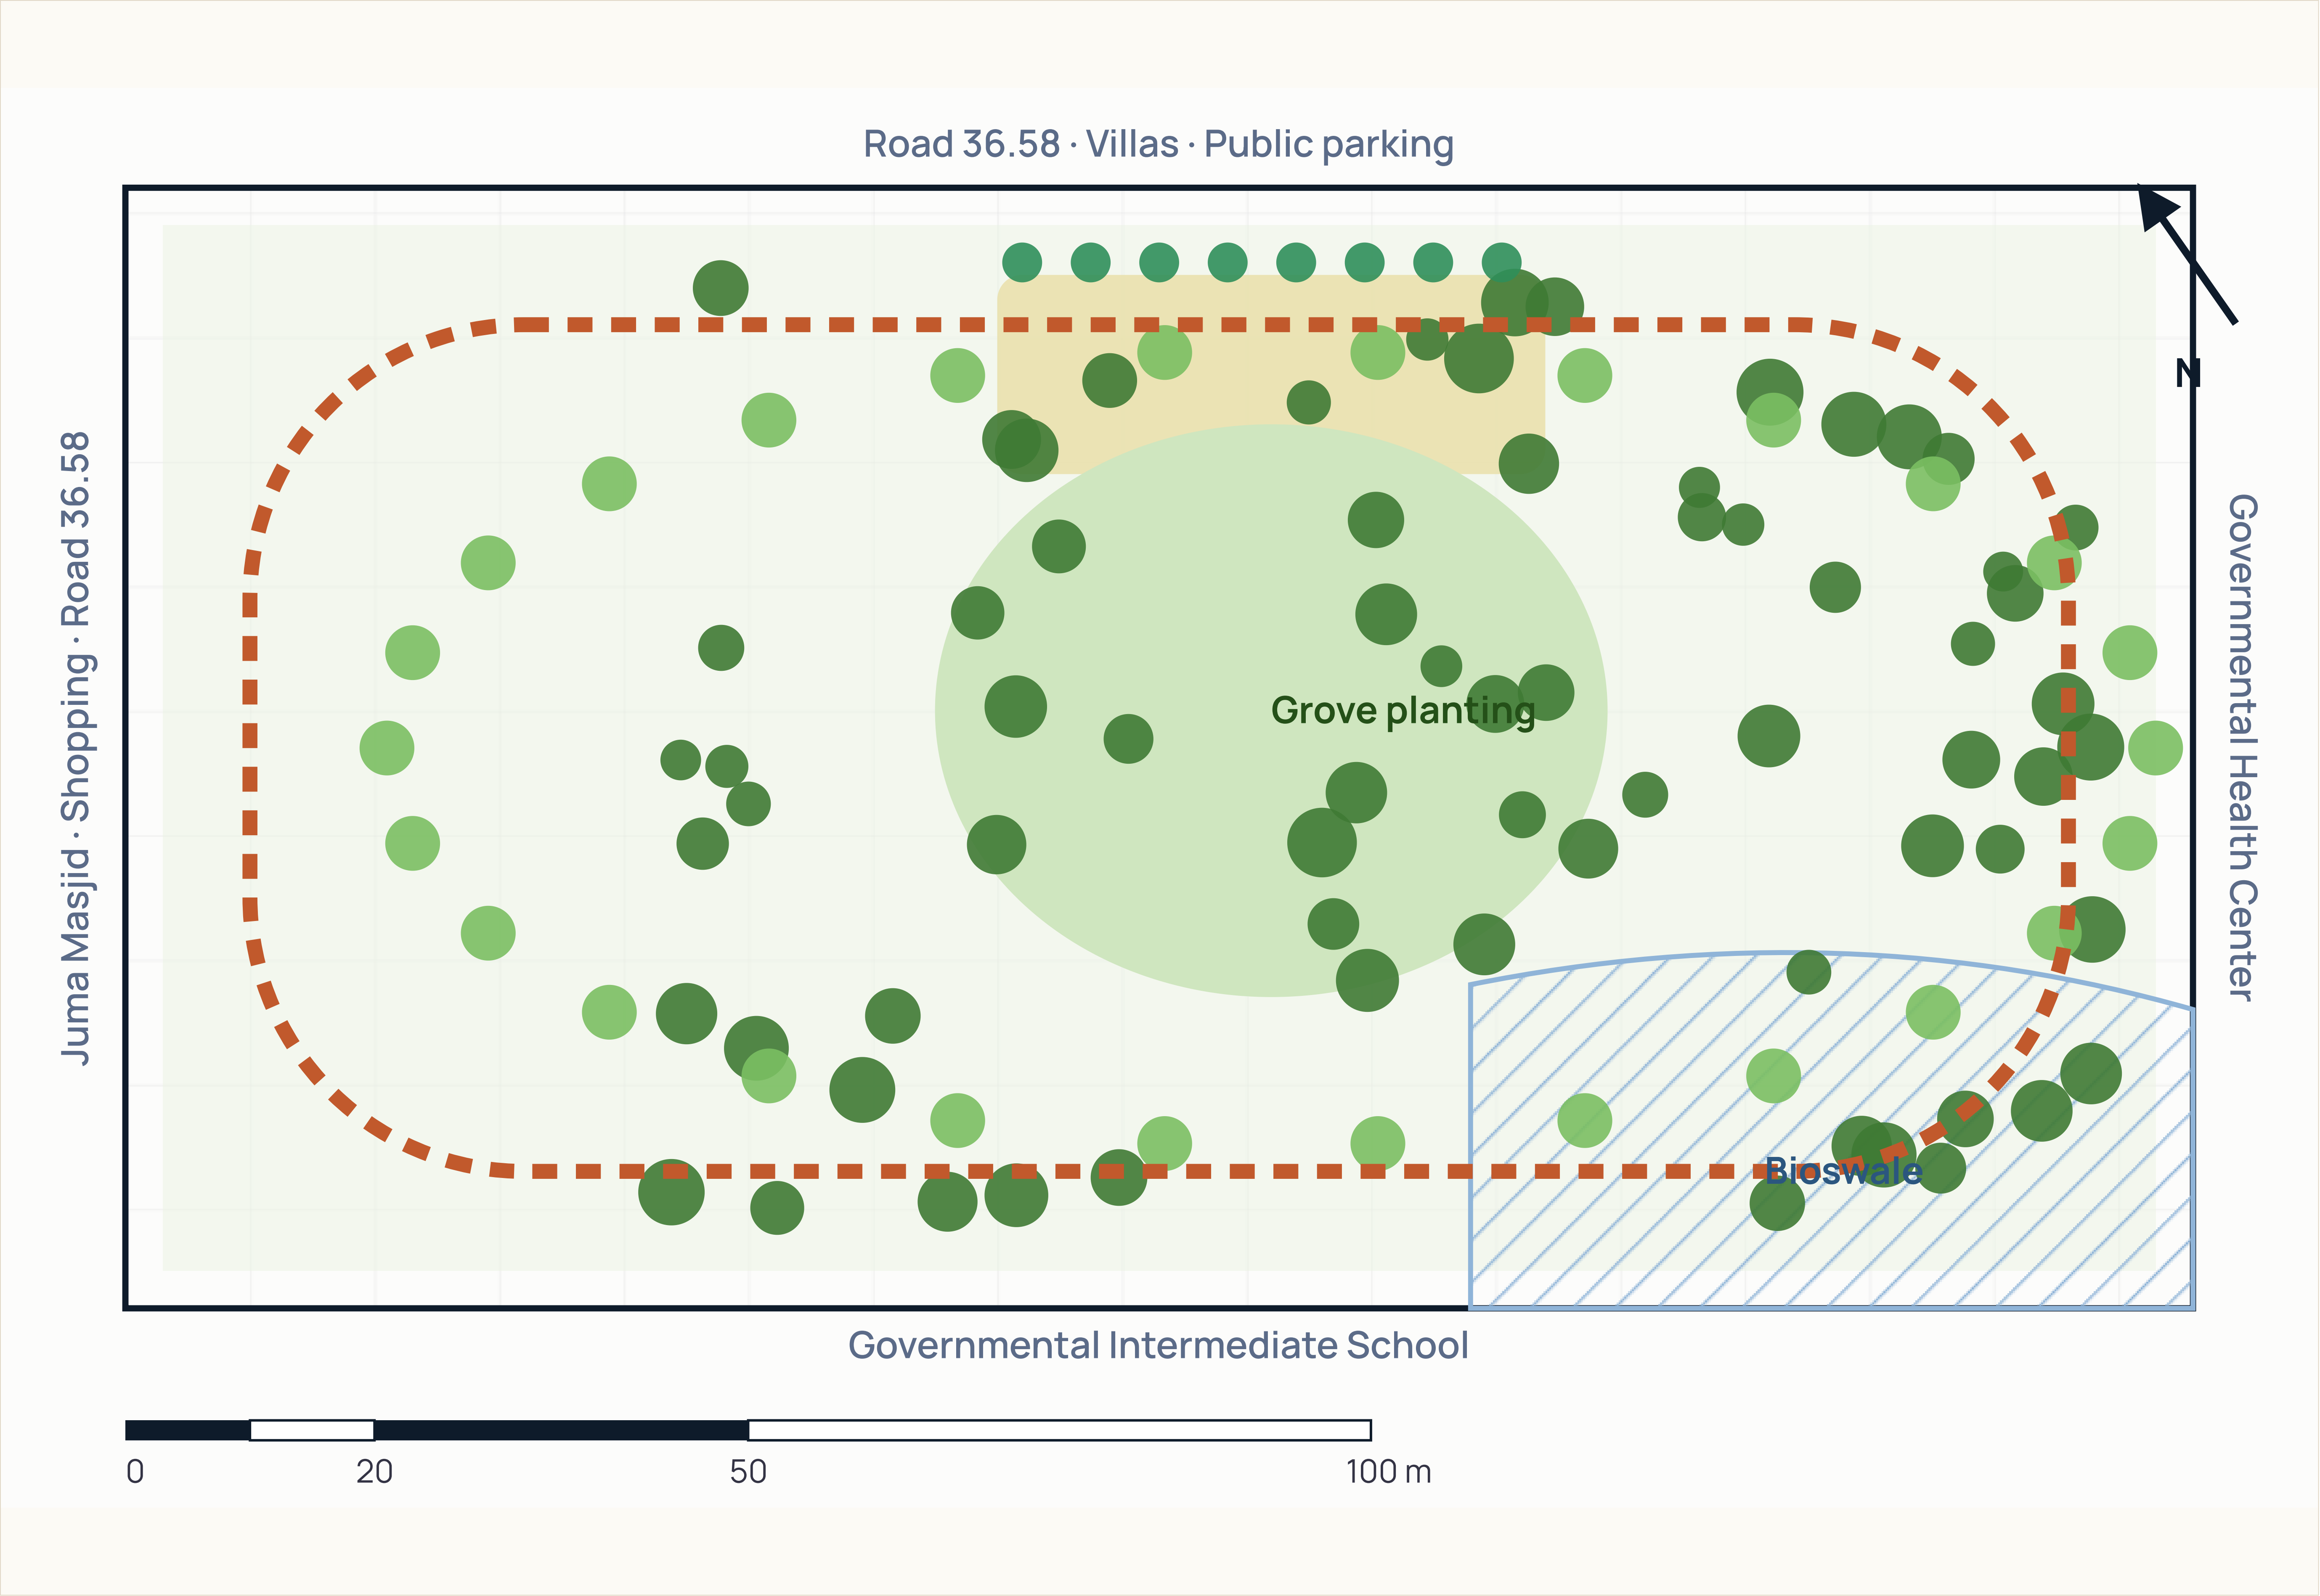

Planting palette

Signature & shade trees

Ghaf (*Prosopis cineraria*) – UAE national tree, deep-rooted, low water

Sidr (*Ziziphus spina-christi*) – dense shade, cultural value

Date Palm (*Phoenix dactylifera*) – avenues & identity

Damas, Neem, Al Marikh – fast canopy & wind buffer

Shrubs & groundcovers

Desert Cassia, Tecoma, Leptadenia, Salvadora

Native grasses & wildflower meadow (seasonal)

Bioswale / Sponge Garden

Halophytes & rain-garden species tolerant of pulse irrigation

Water strategy

Xeriscape zoning · subsurface drip · AC-condensate & treated greywater harvesting · bioswales for stormwater

· soil-moisture sensors. **Irrigation demand ~41%** vs. a conventional turf park.

Legend

Existing mature tree (retained)

New shade / signature tree


Shrub & groundcover beds

Native meadow / lawn

Bioswale / rain garden


SECTION A-A · Cool Loop & solar pergola


Scale 1:100 @ A1

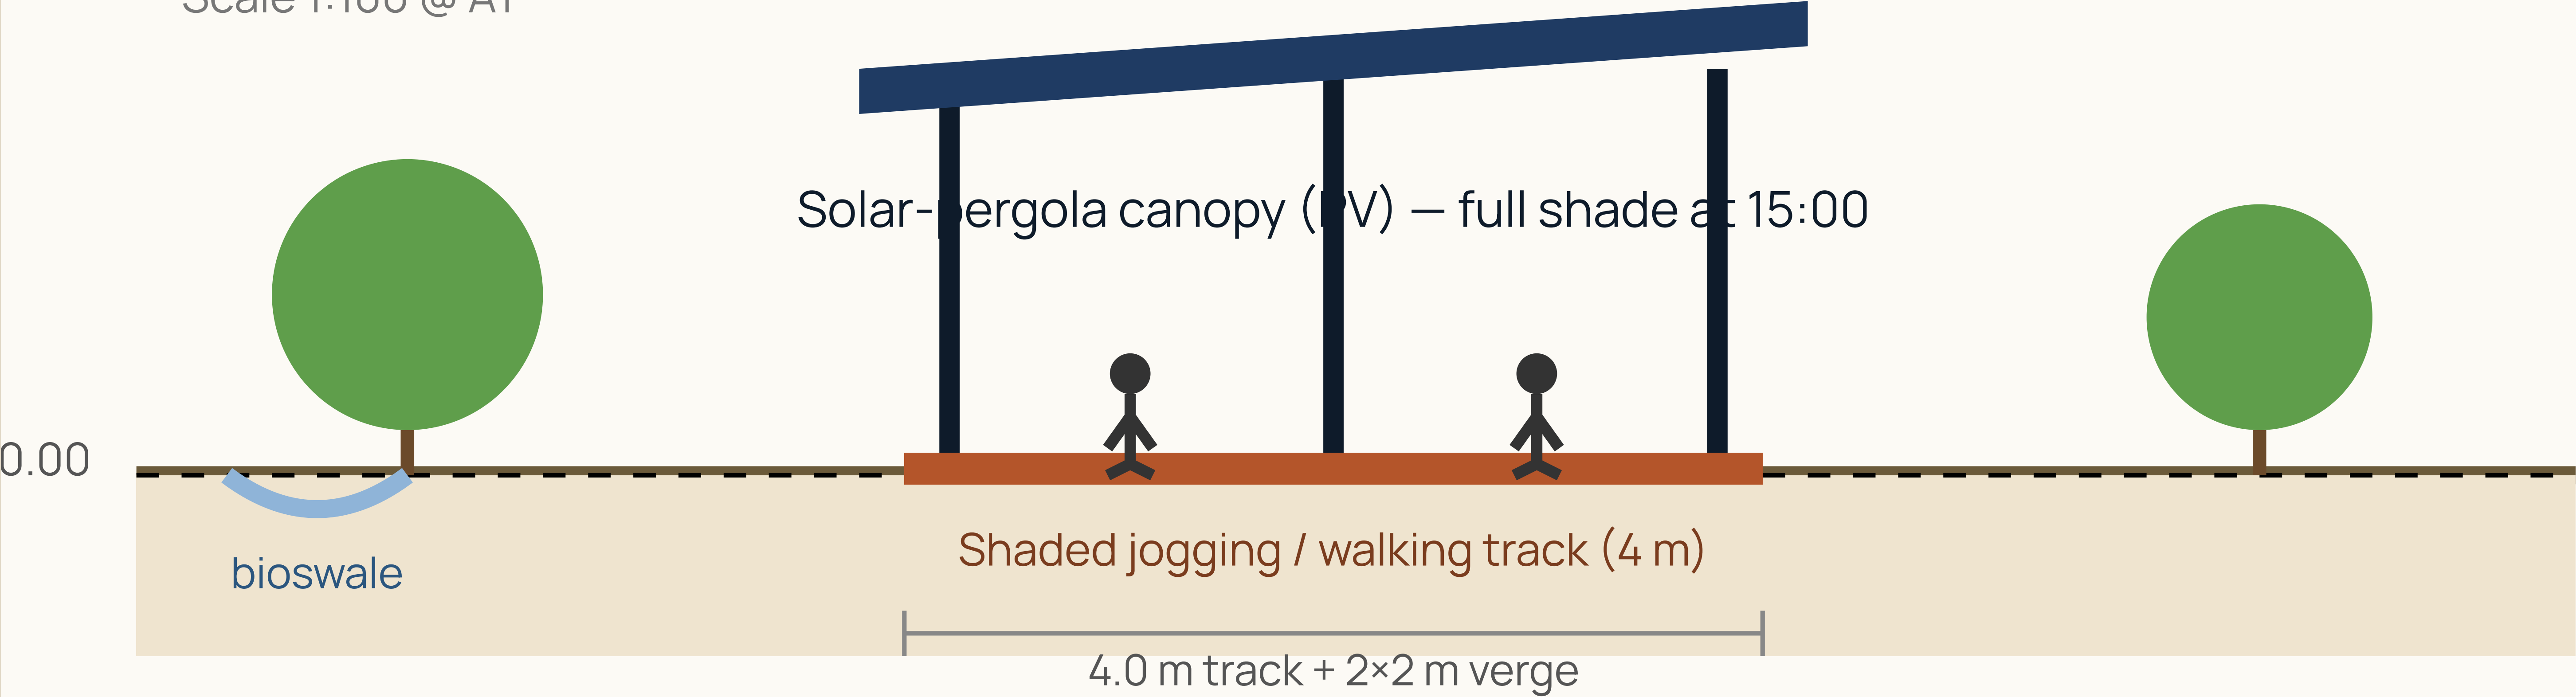

SECTION B-B · Majlis Grove (social core)

Scale 1:100 @ A1

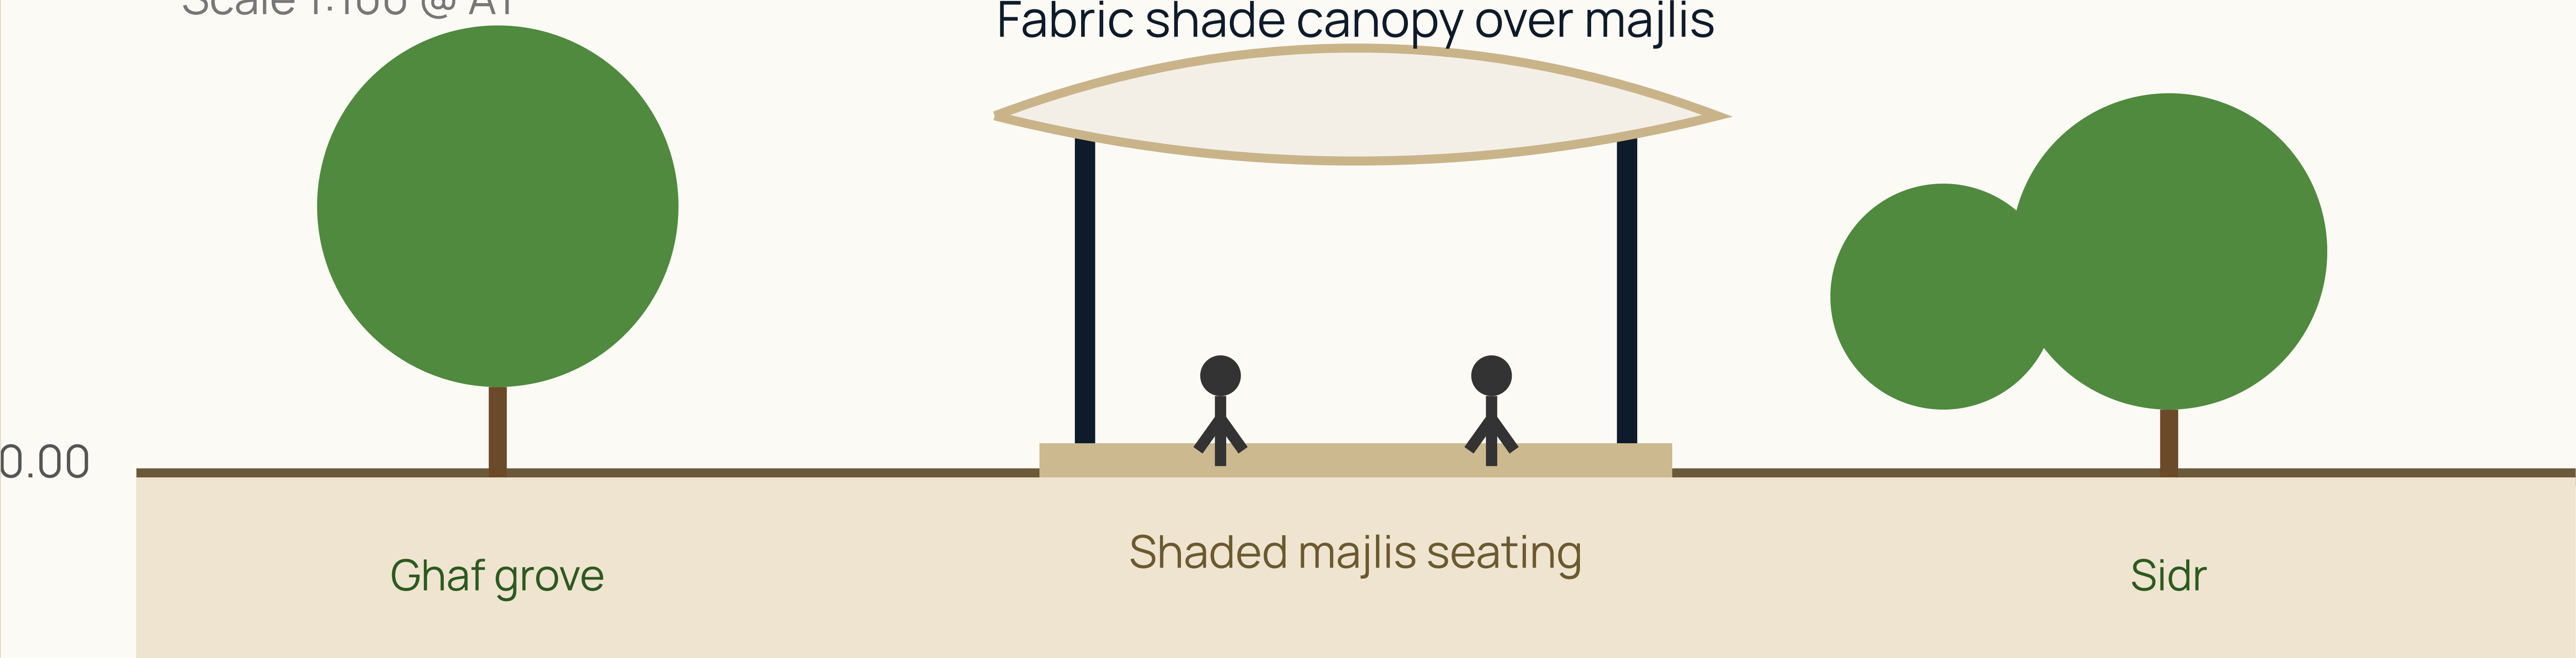

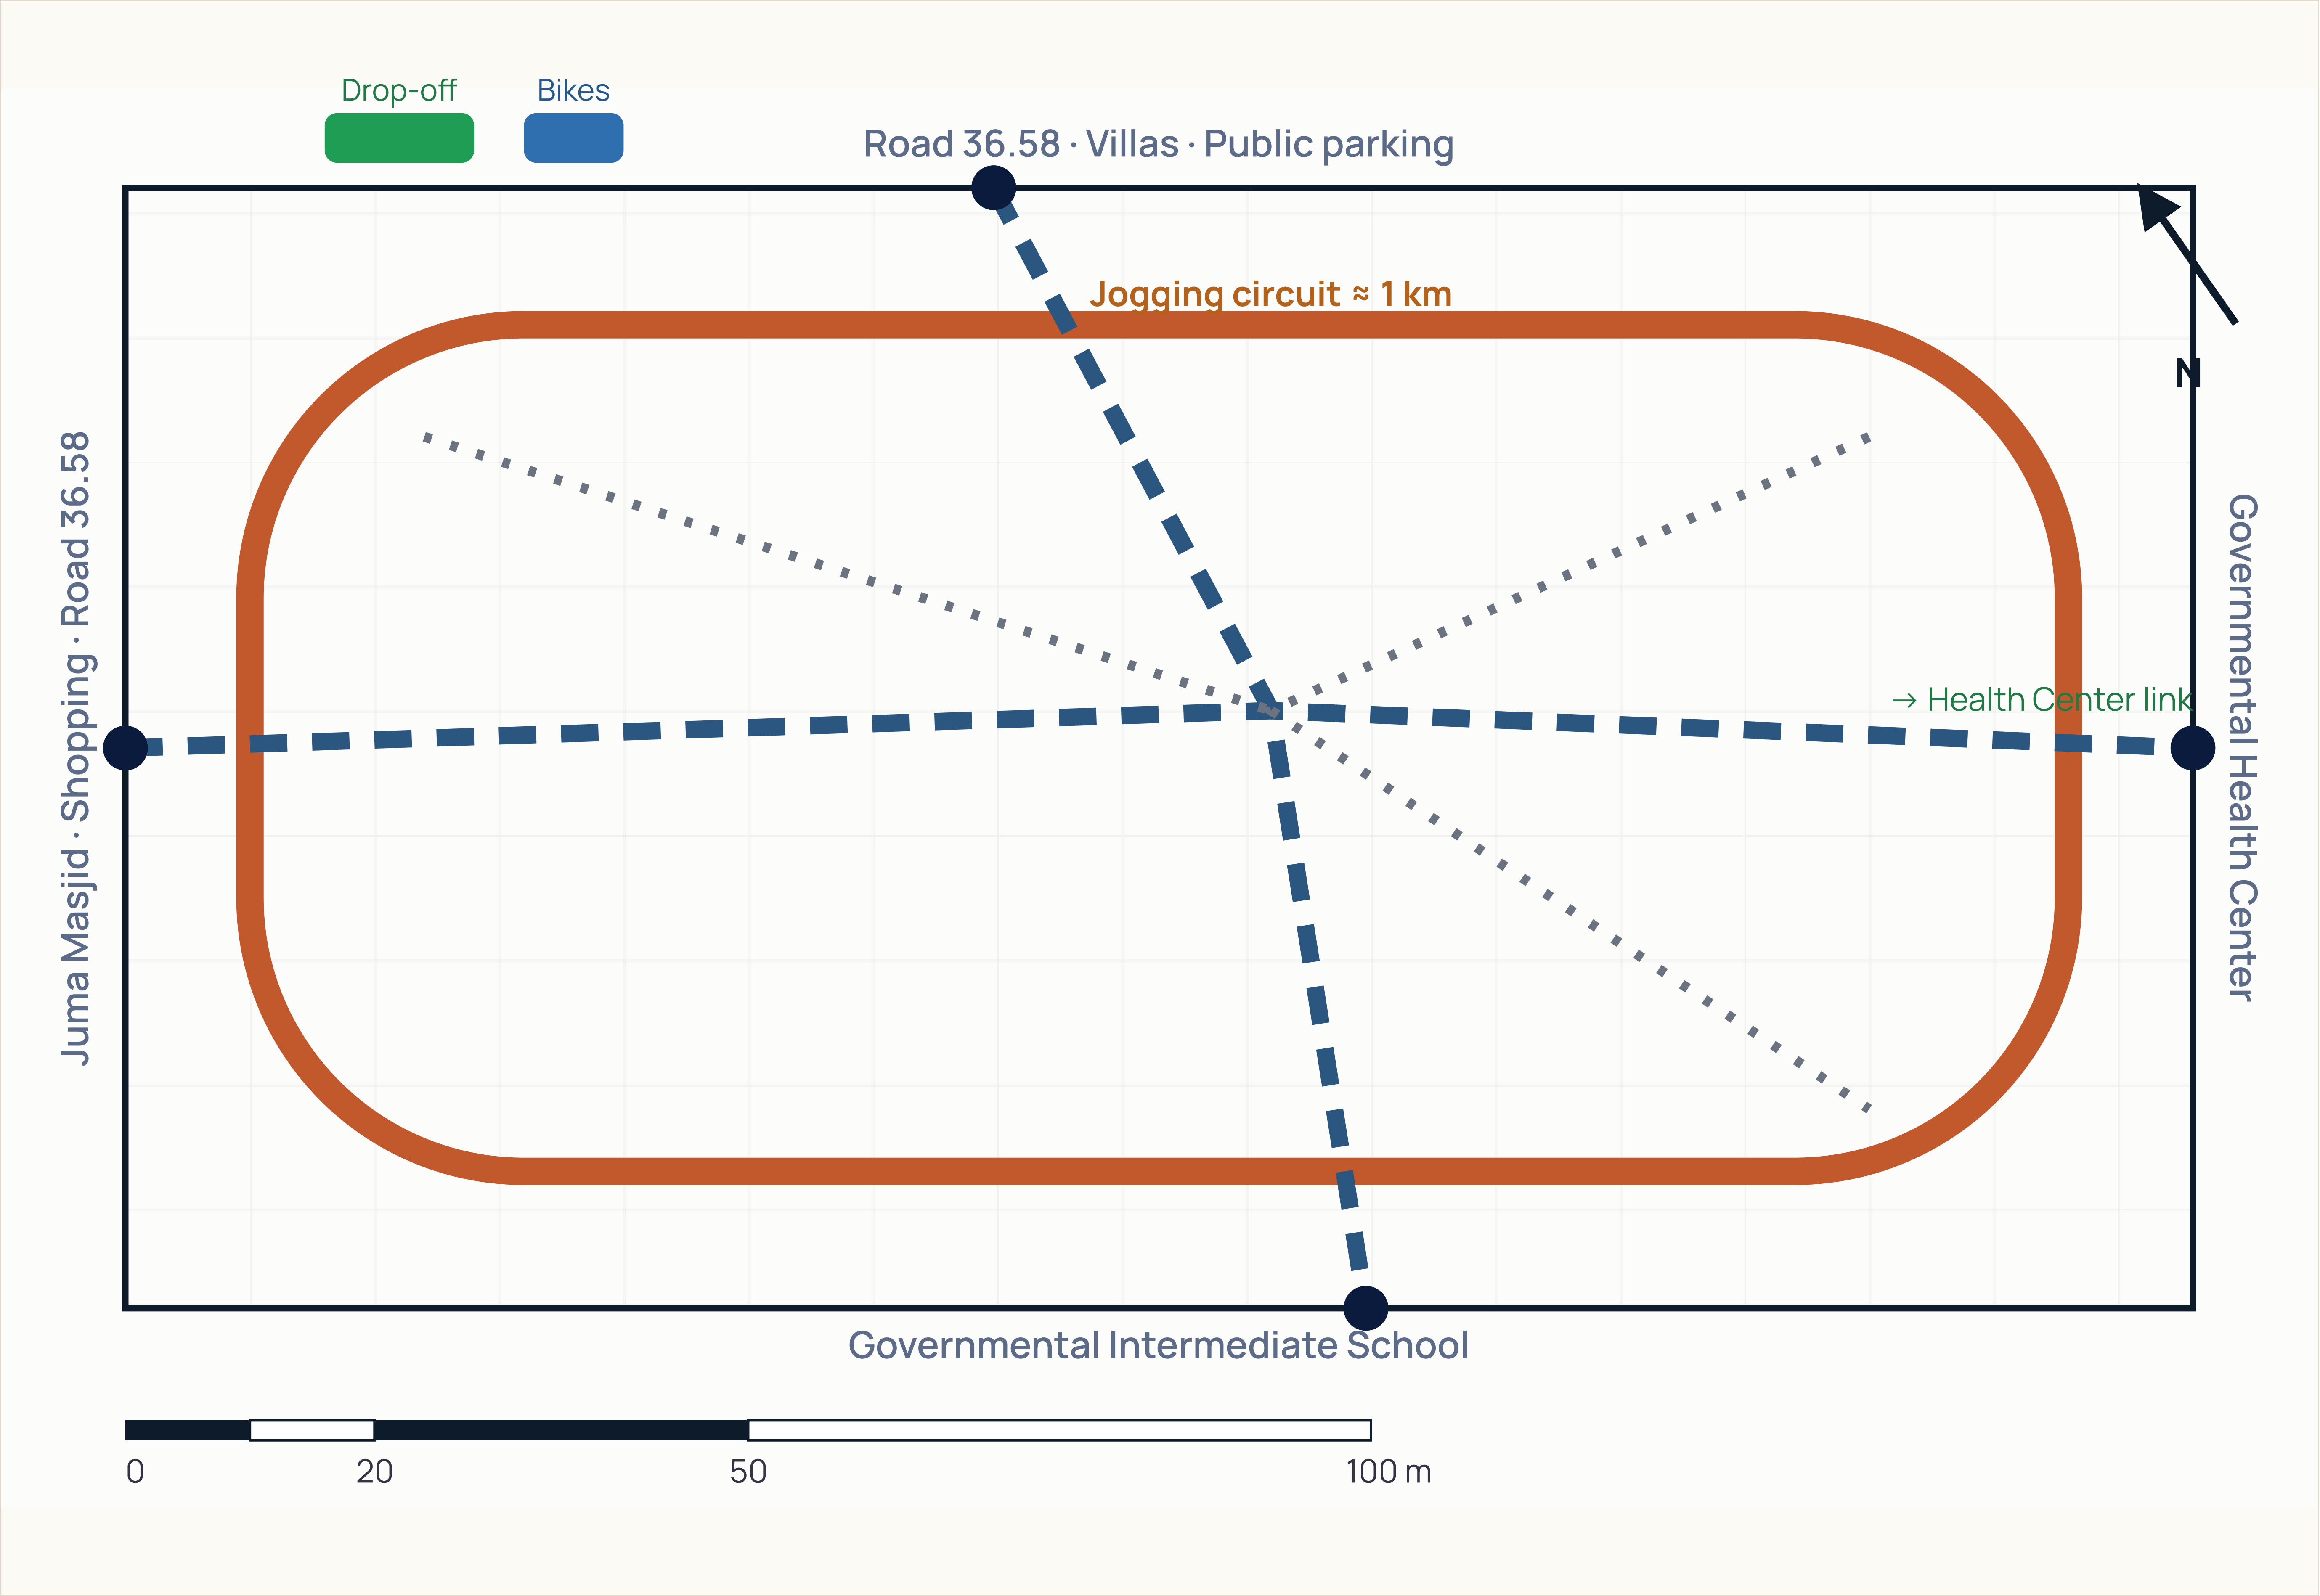

Access & mobility

- Jogging circuit ≈ 1 km (shaded)
- Primary promenade (step-free)
- Secondary paths
- Gateway entrance (×4)
- Accessible drop-off
- Bicycle parking

Universal design

All primary routes step-free, max 1:20 gradient, tactile paving & rest nodes ≤ 60 m apart, high-contrast bilingual wayfinding, shaded seating along the loop, accessible WCs and an all-abilities playground — designed to national & international accessibility standards for People of Determination.

Direct step-free link to the Governmental Health Center gateway.