



ZILAL AL SAFA — CONCEPT MASTERPLAN

Al Safa Park 2 Redevelopment · Plot 3570616 · 15,000 m² · Dubai Municipality AI Park Design Challenge

Drawing L-101 · Masterplan
Scale 1:250 @ A1 · North ↑ true
Rev A · Concept + Preliminary

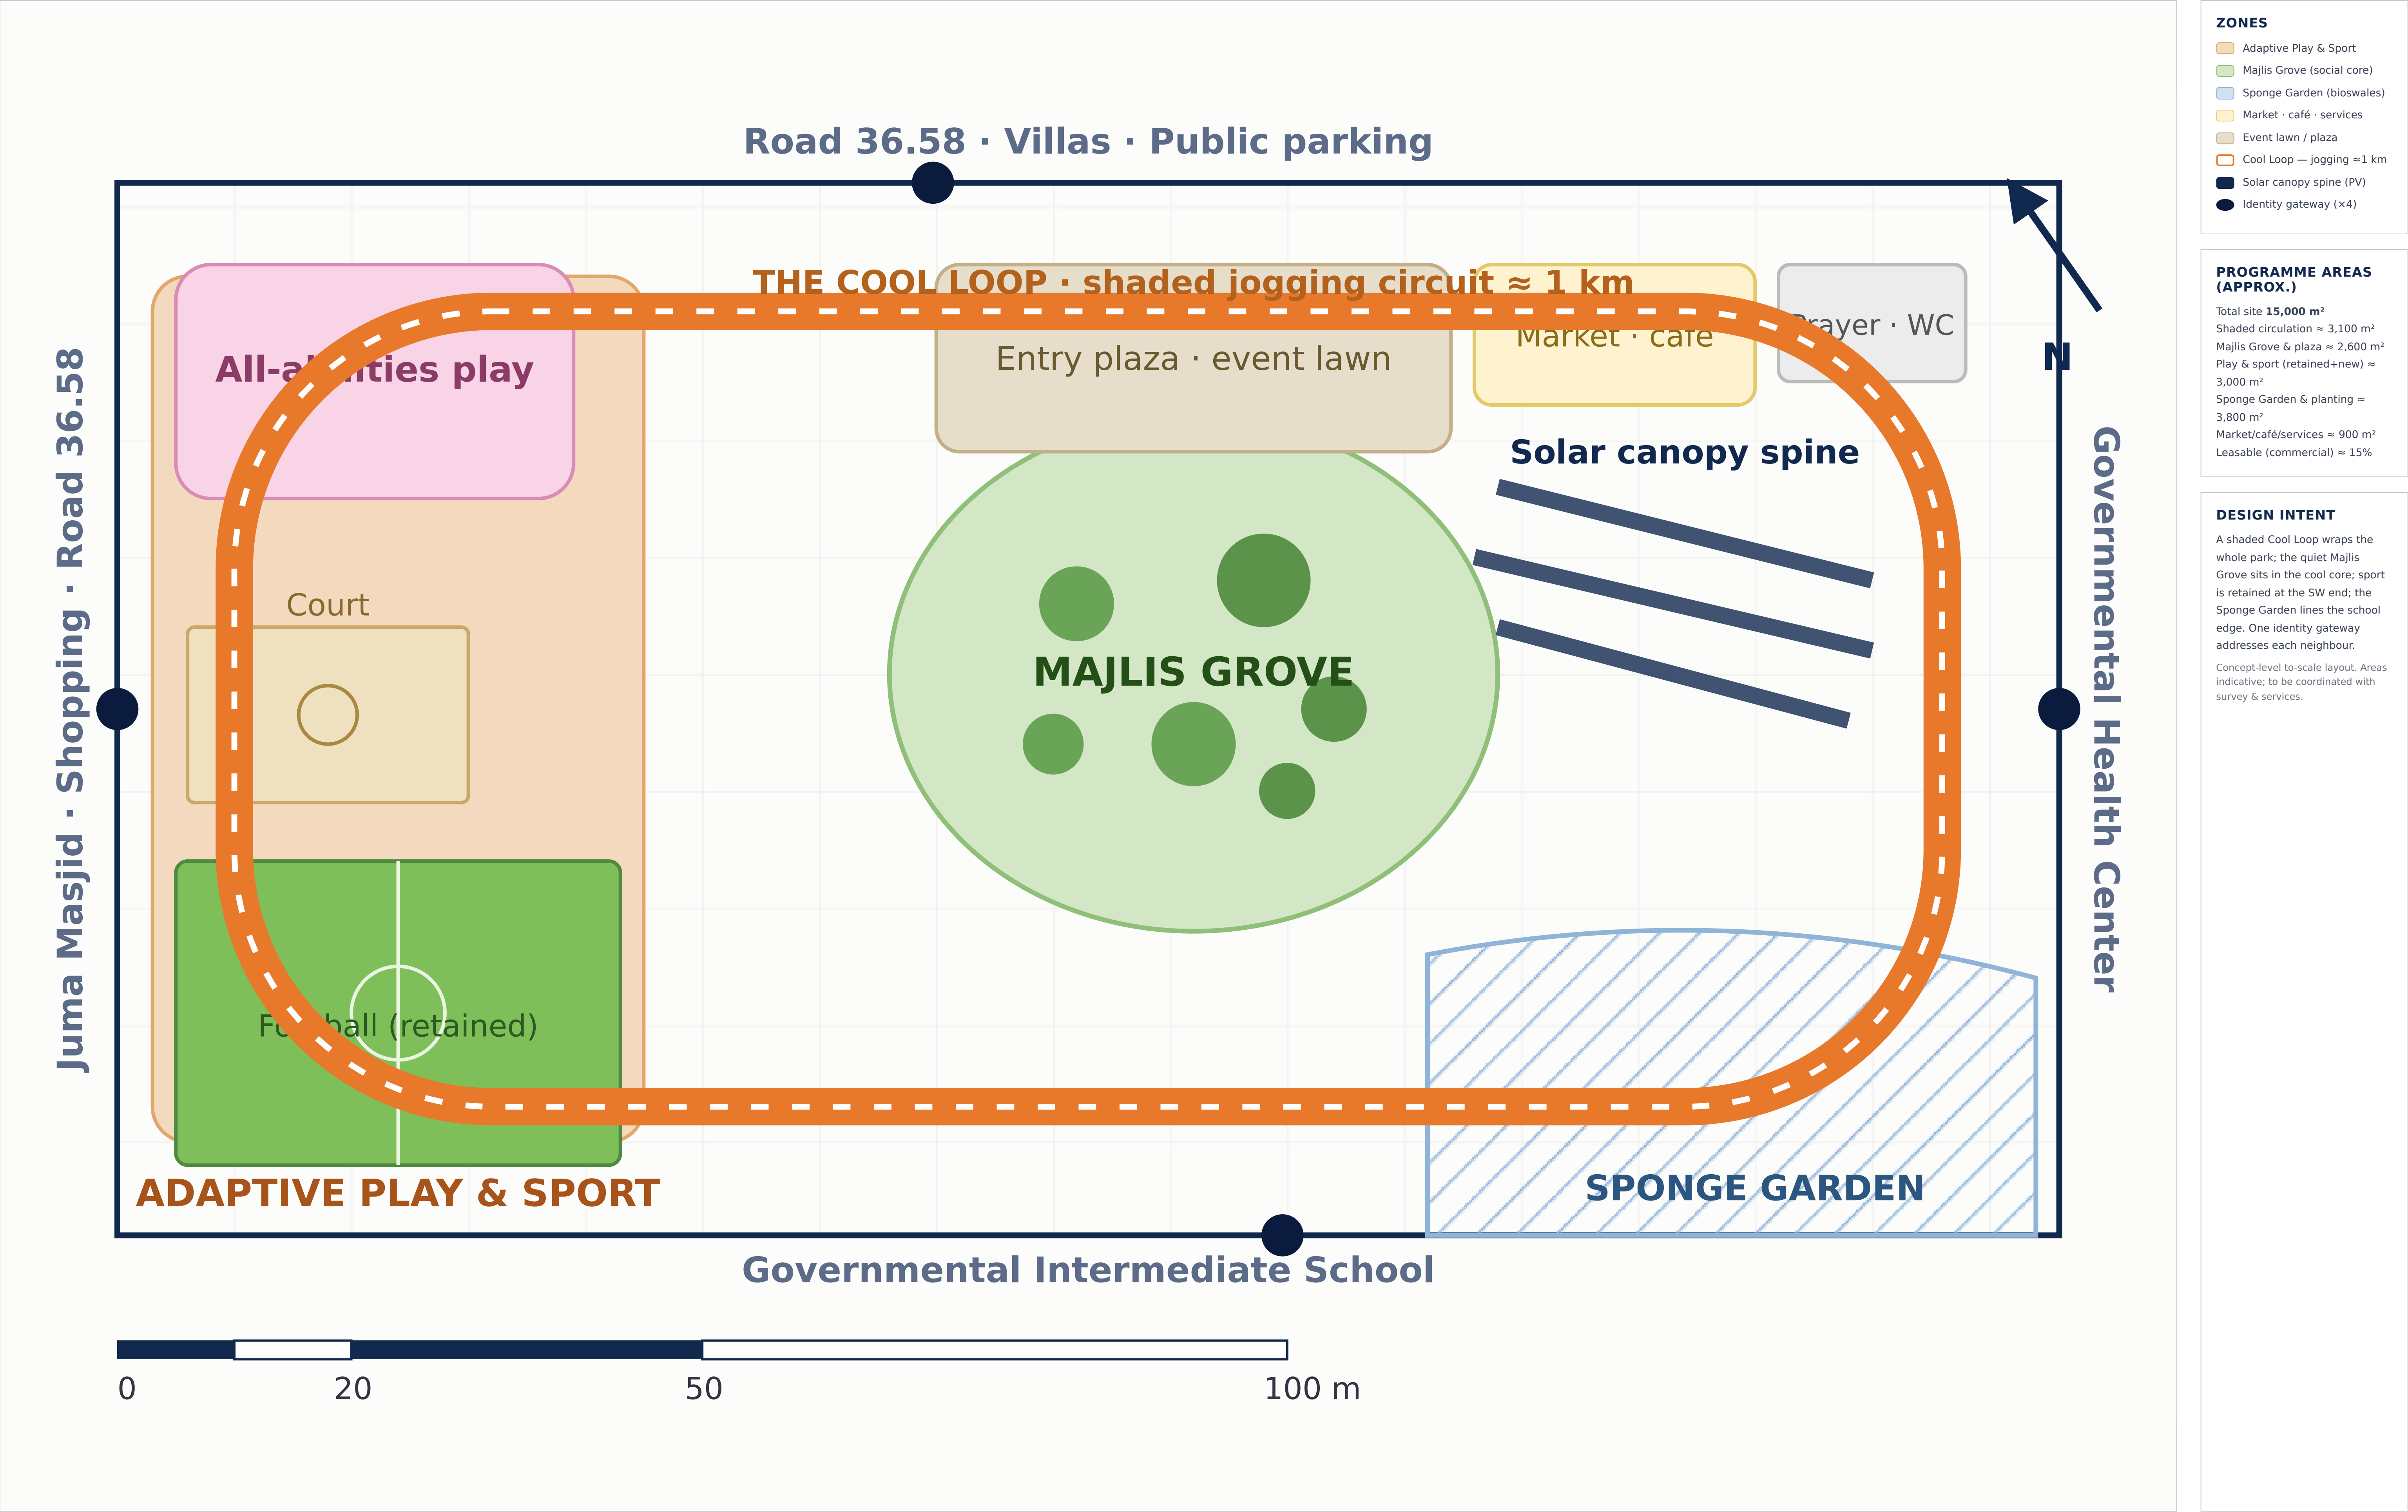

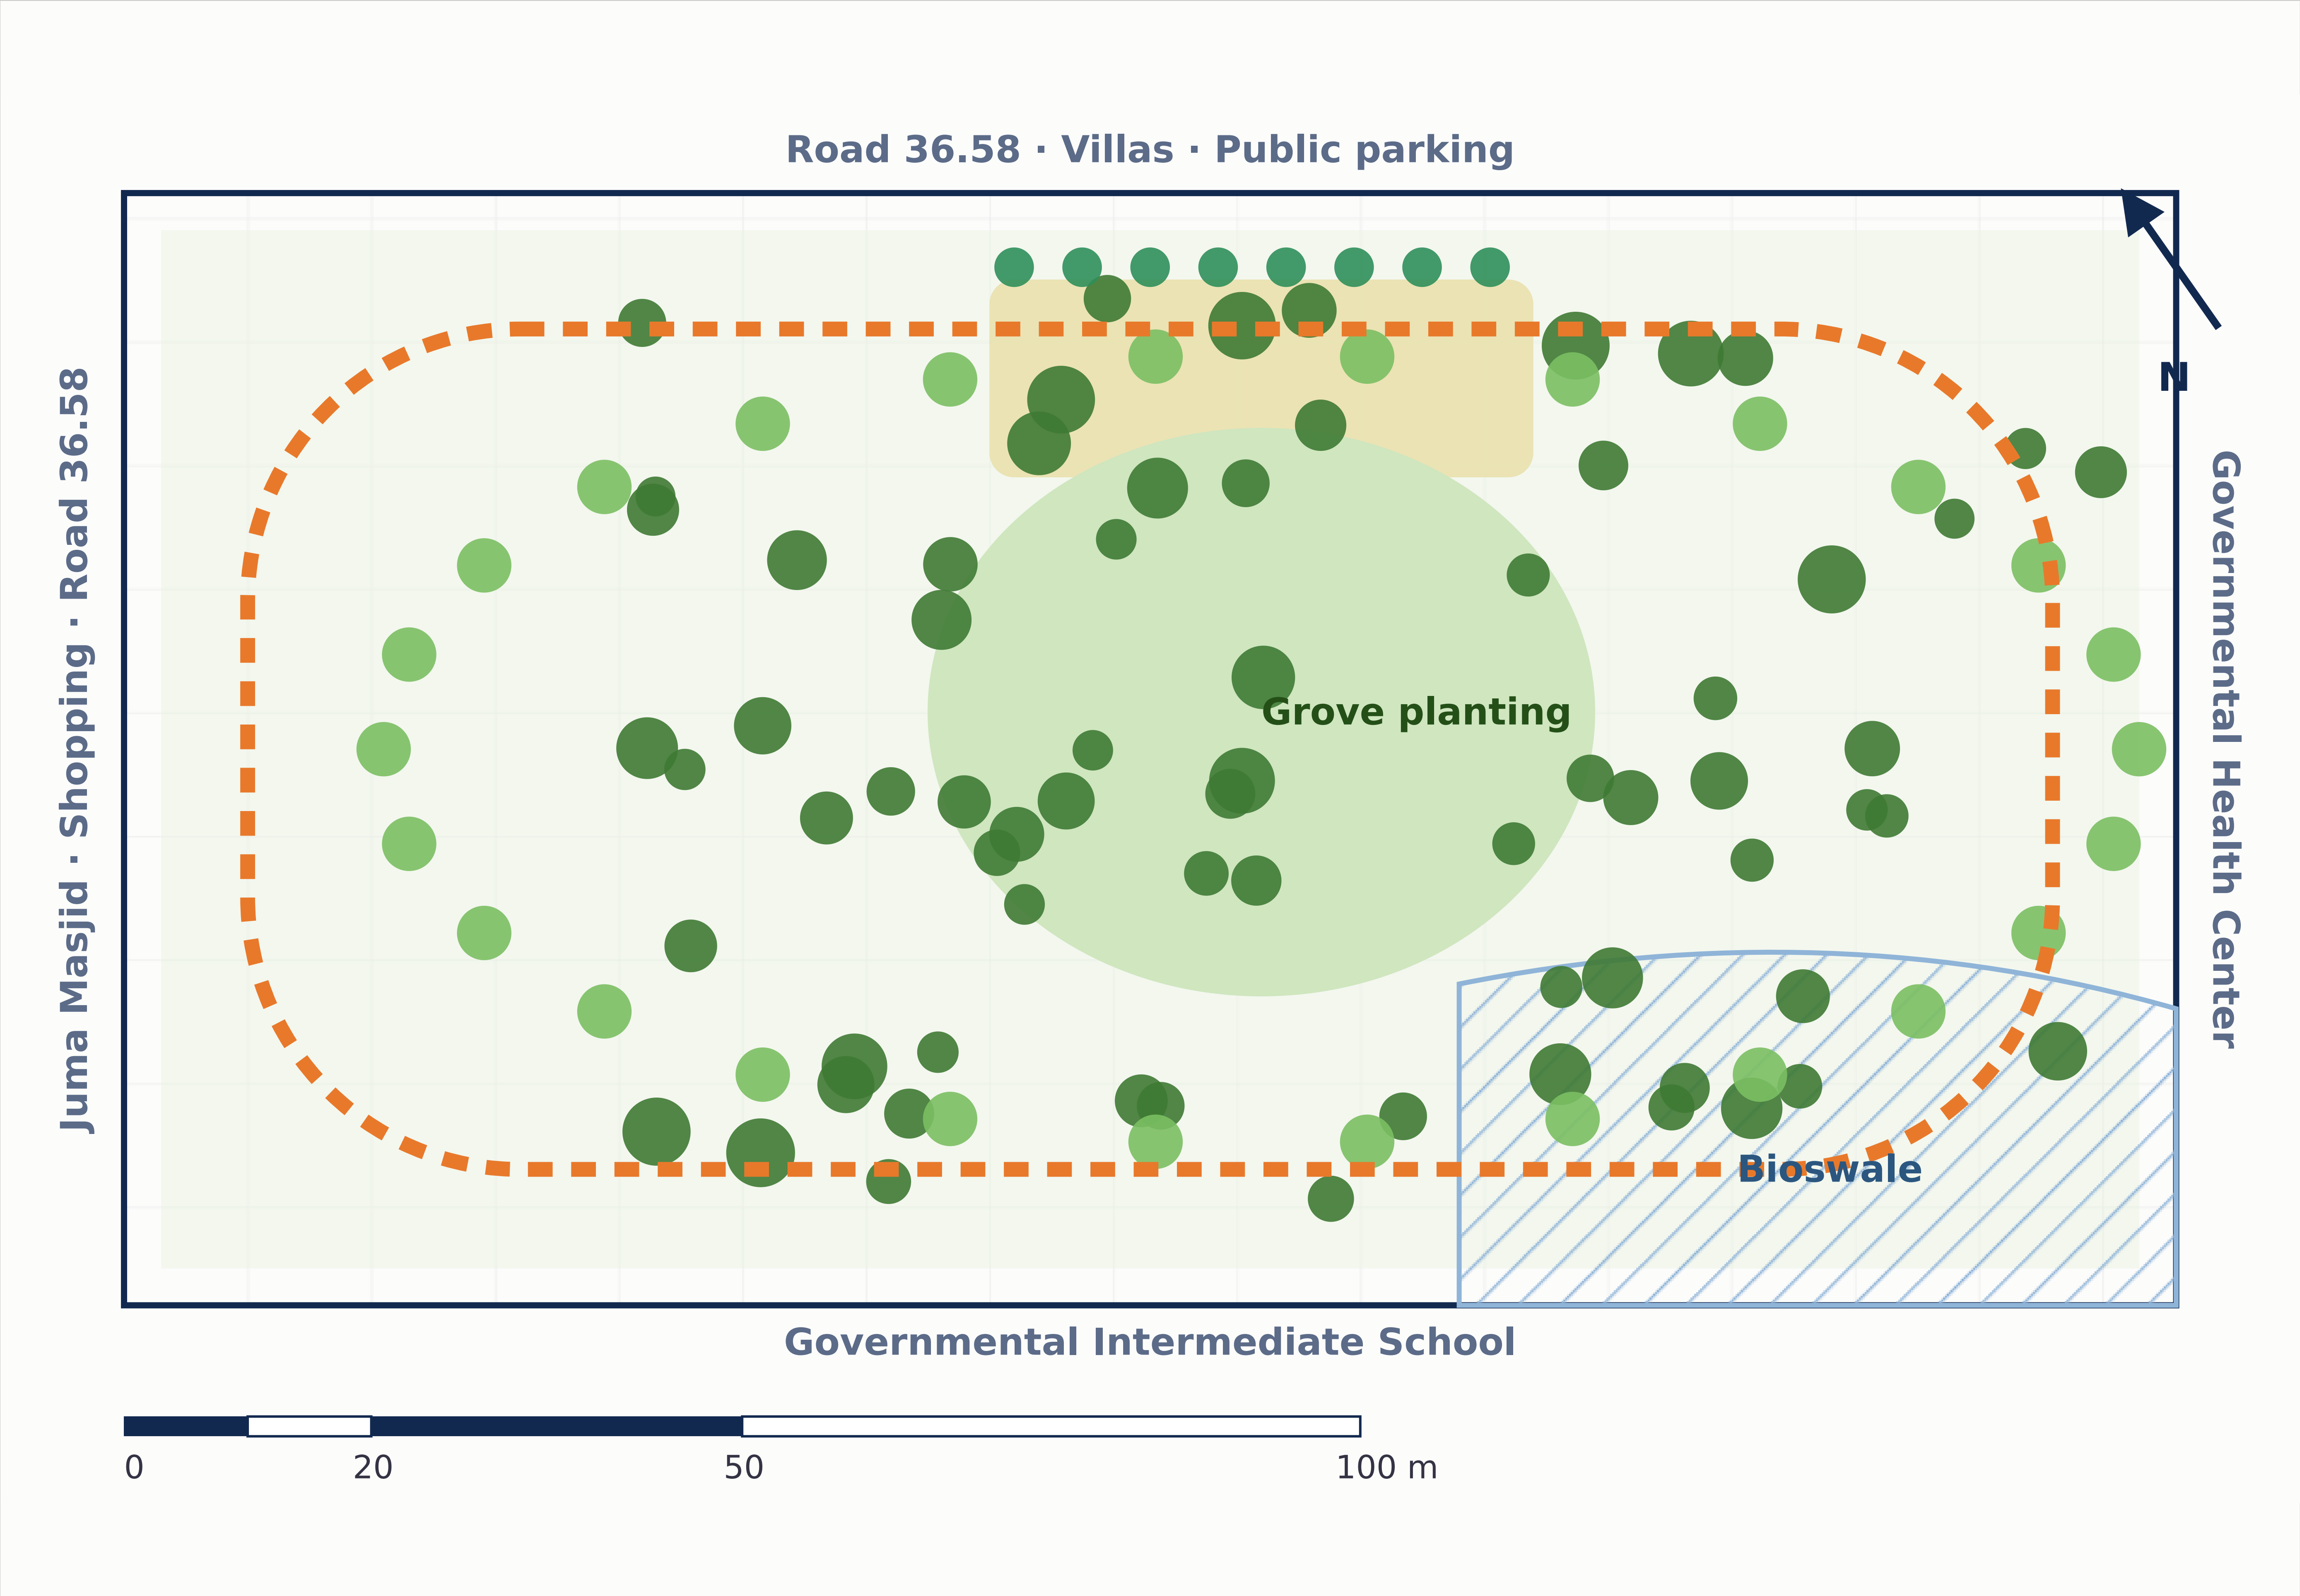

PLANTING PALETTE

Signature & shade trees

Ghaf (*Prosopis cineraria*) — UAE national tree, deep-rooted, low water

Sidr (*Ziziphus spina-christi*) — dense shade, cultural value

Date Palm (*Phoenix dactylifera*) — avenues & identity

Damas, Neem, Al Markh — fast canopy & wind buffer

Shrubs & groundcovers

Desert Cassia, Tecoma, Leptadenia, Salvadoria

Native grasses & wildflower meadow (seasonal)

Bioswale / Sponge Garden

Halophytes & rain-garden species tolerant of pulse irrigation

WATER STRATEGY


Xeriscape zoning · subsurface drip · AC-condensate & treated greywater harvesting · bioswales for stormwater · soil-moisture sensors. **Irrigation demand —41%** vs. a conventional turf park.

LEGEND

- Existing mature tree (retained)
- New shade / signature tree
- Shrub & groundcover beds
- Native meadow / lawn
- Bioswale / rain garden


SECTION A-A · Cool Loop & solar pergola

Scale 1:100 @ A1

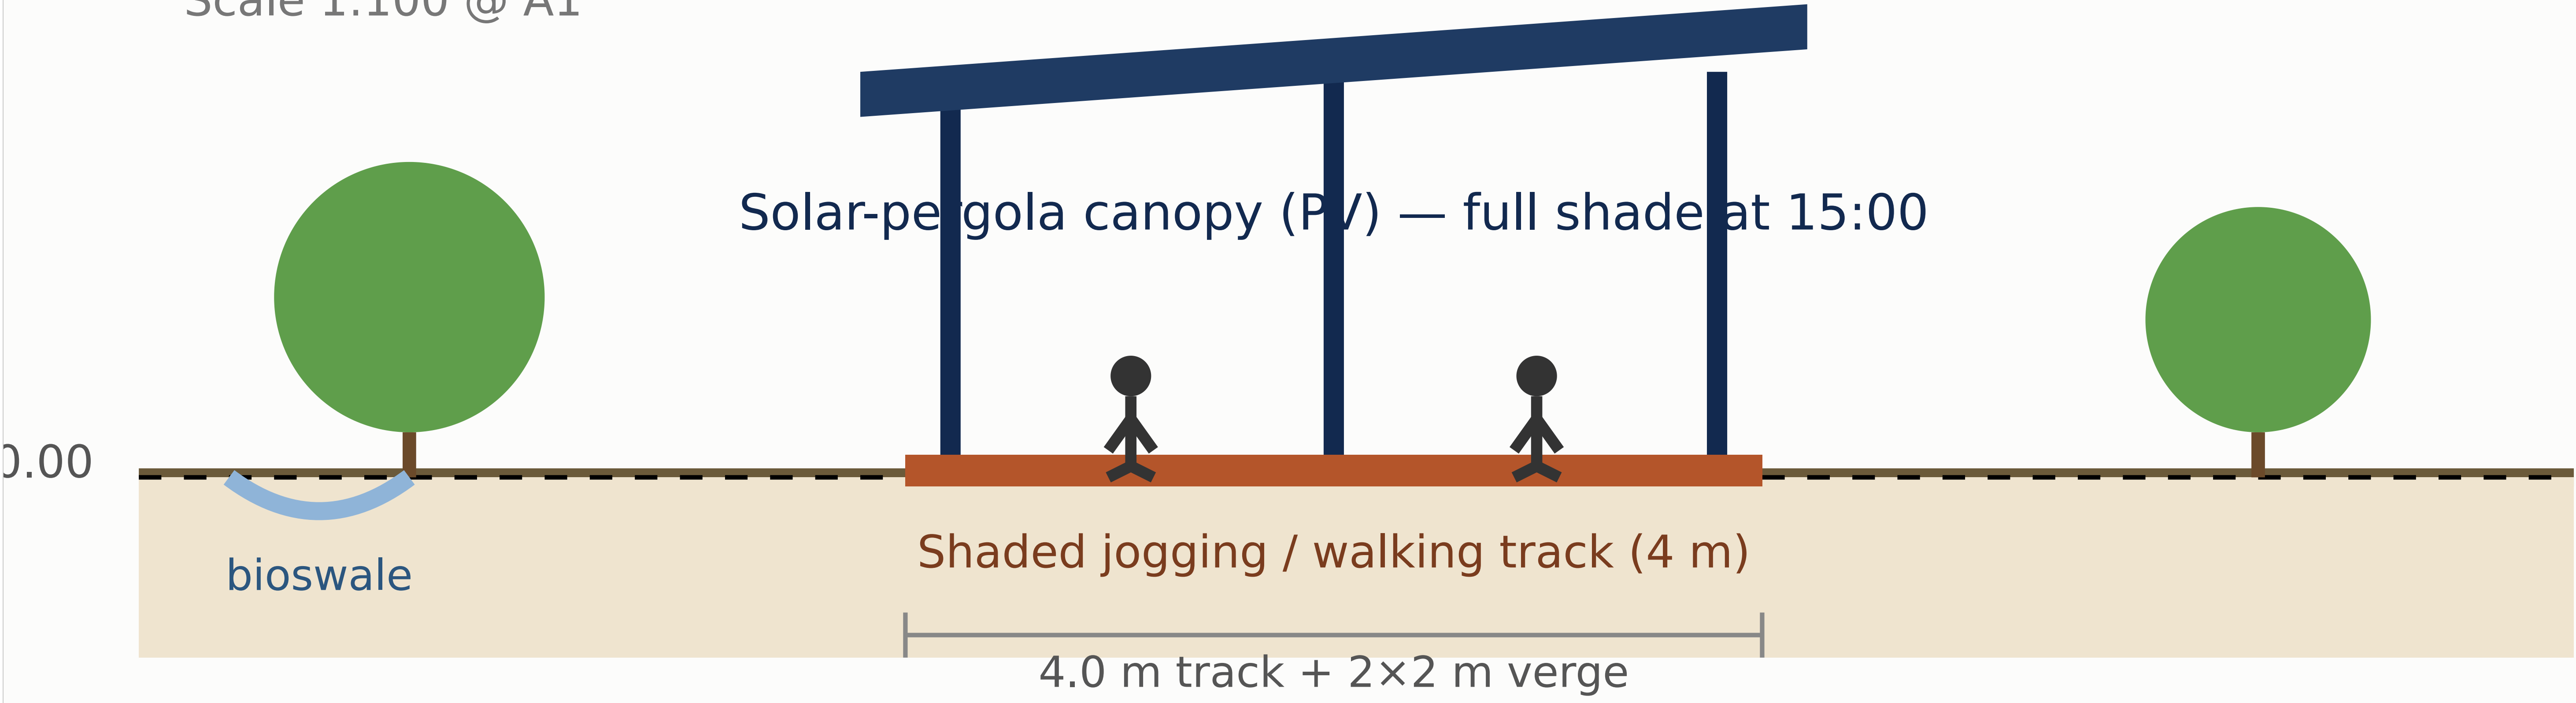


SECTION B-B · Majlis Grove (social core)

Scale 1:100 @ A1

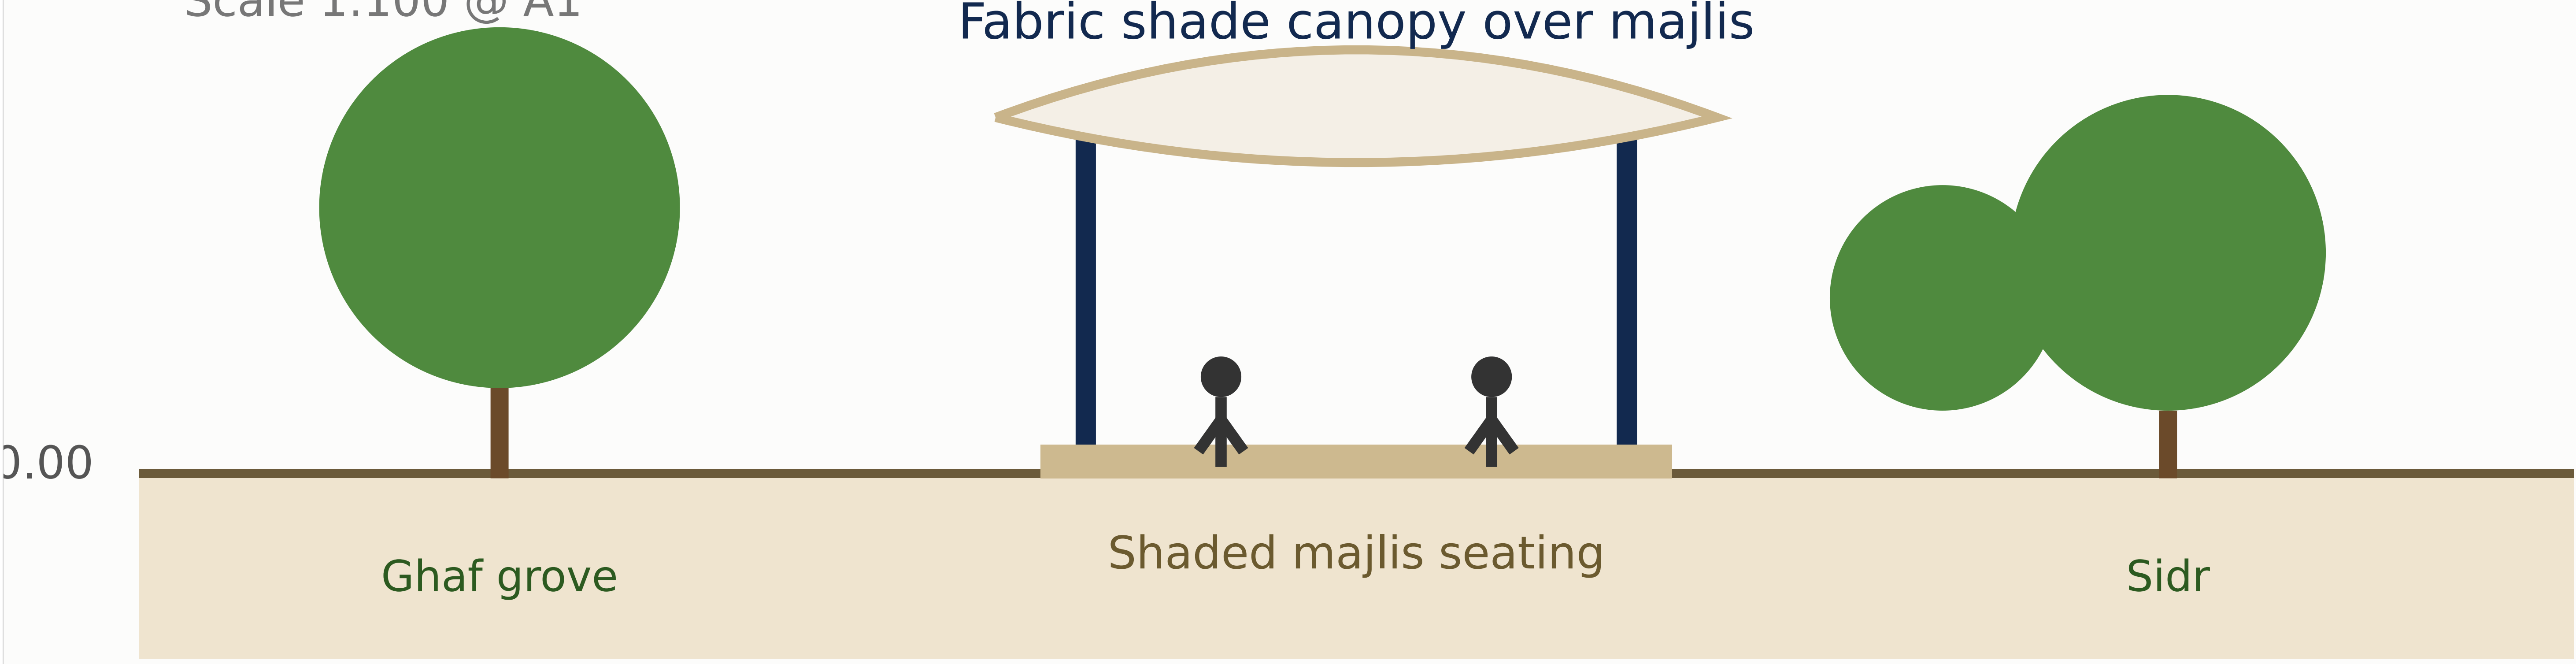

CIRCULATION & ACCESSIBILITY

Step-free network · entrances · jogging circuit · mobility, drop-off & parking

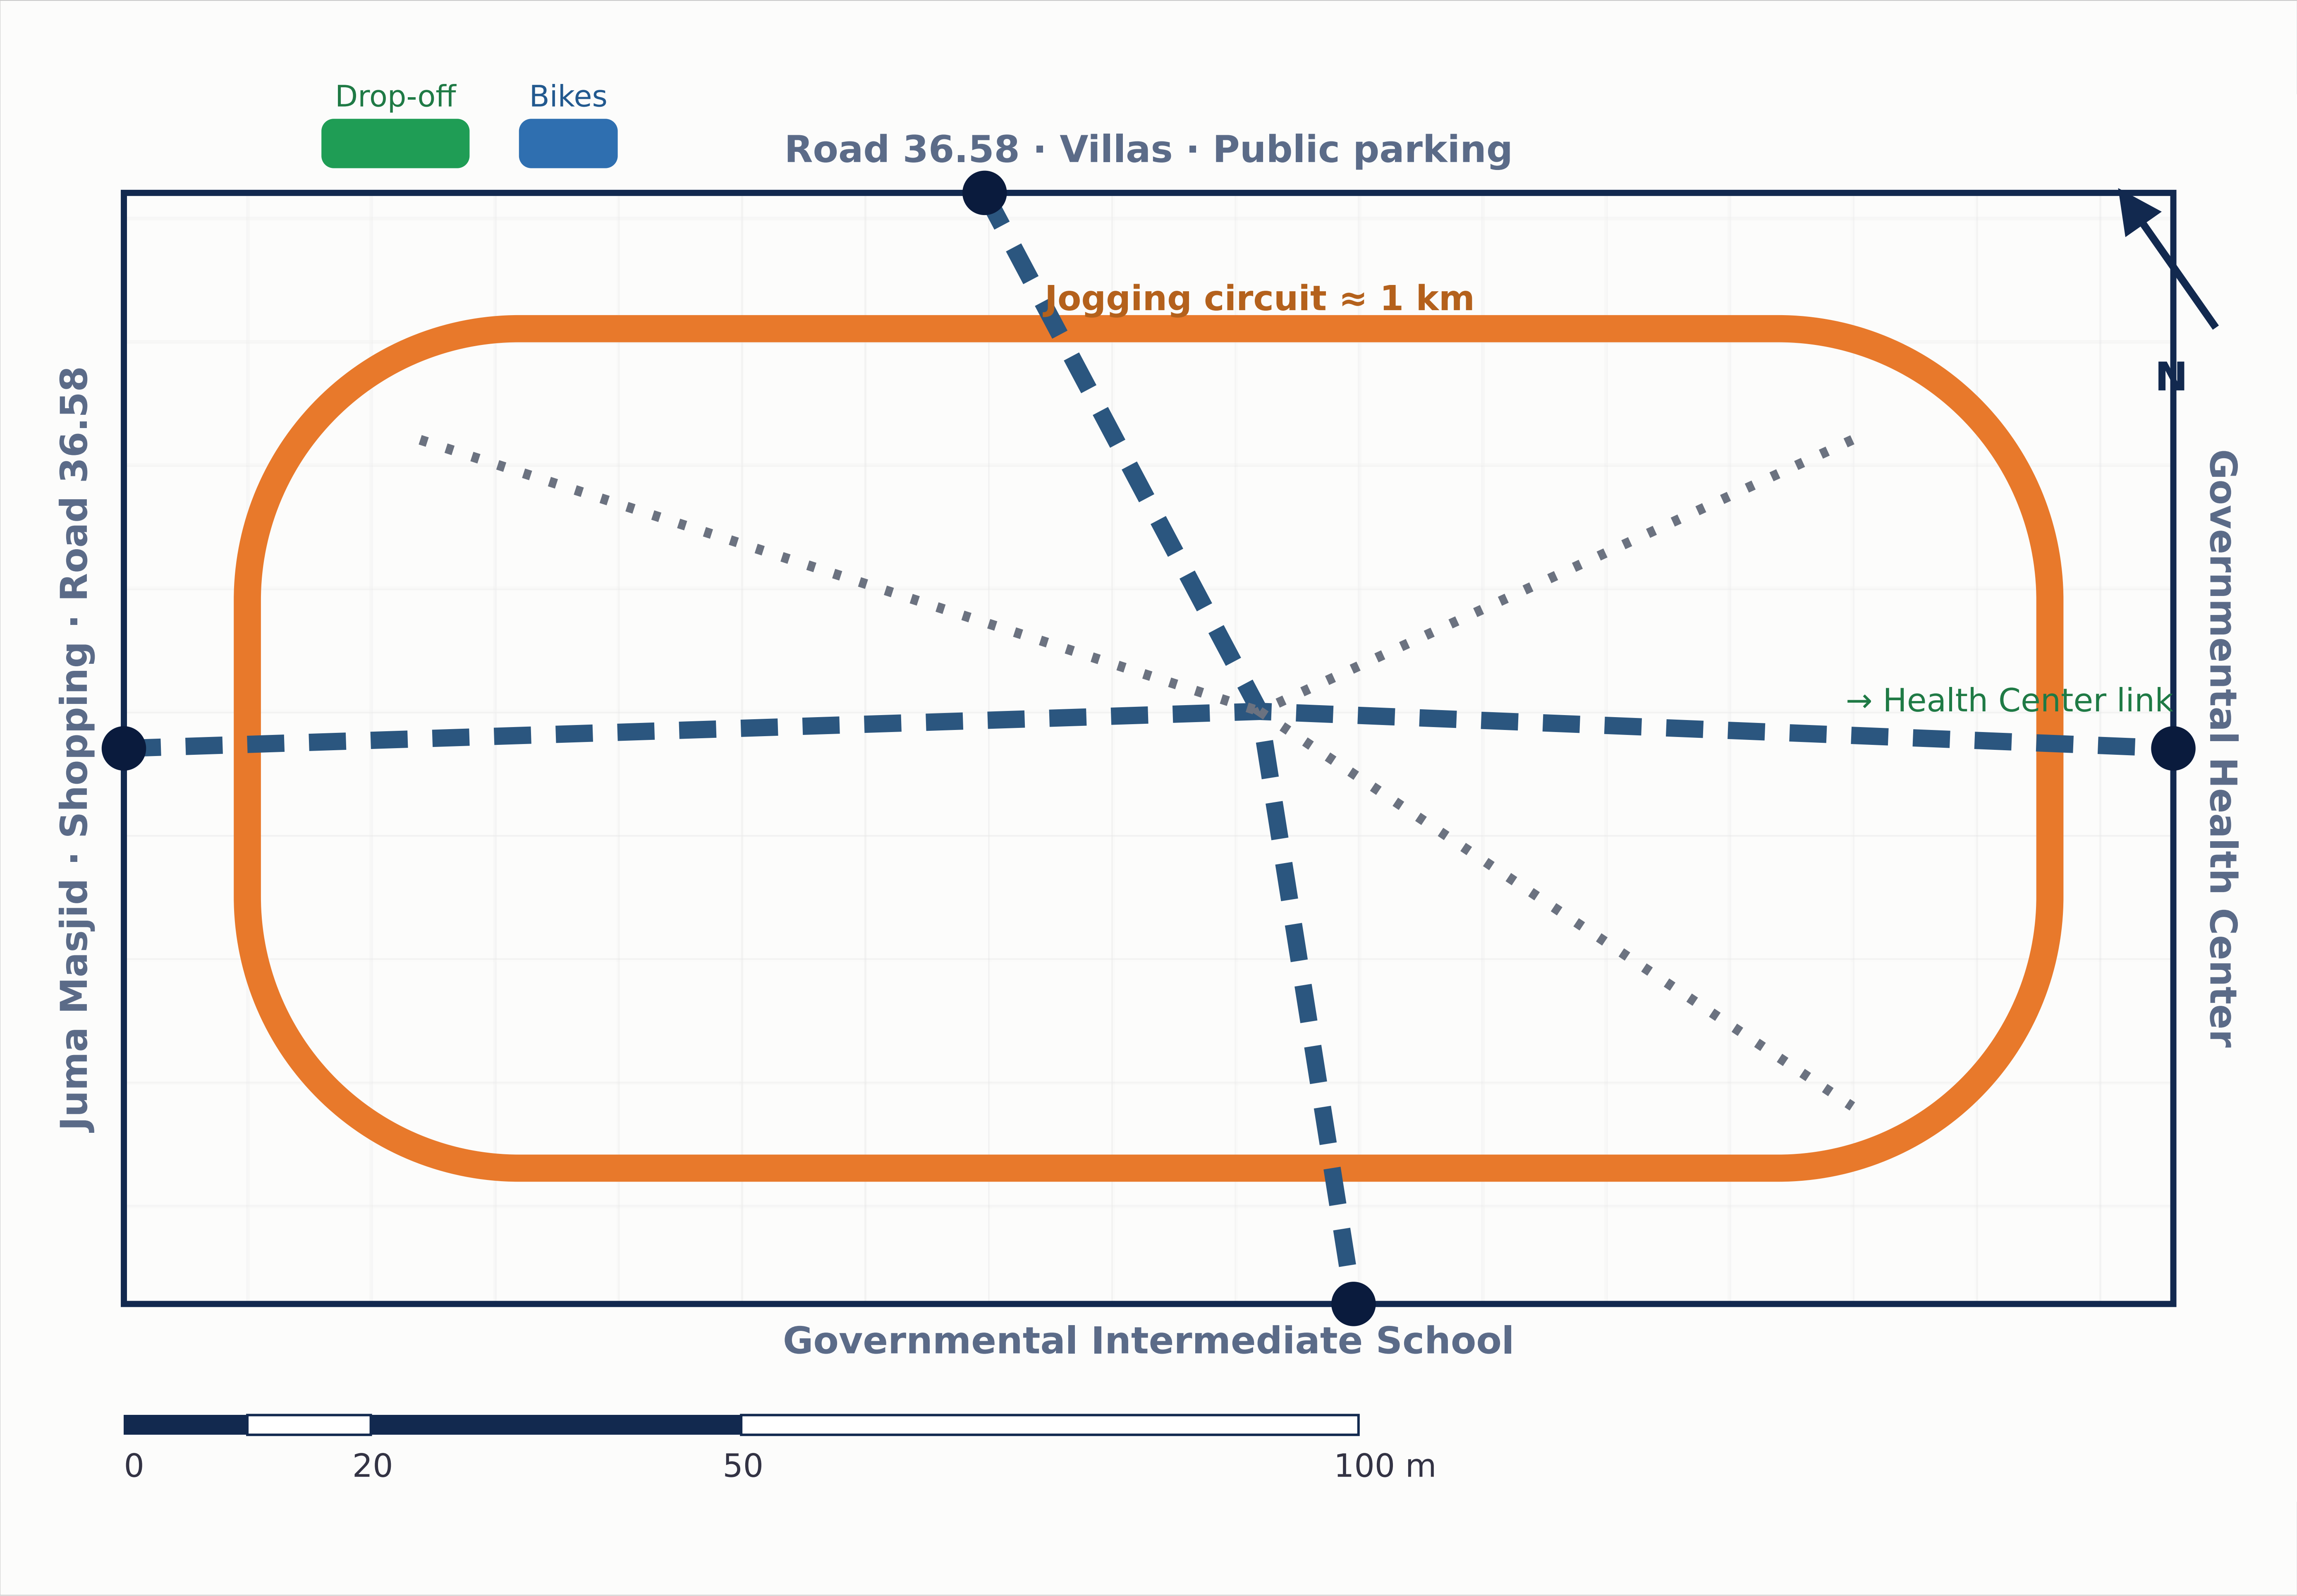

ACCESS & MOBILITY

- Jogging circuit ≈ 1 km (shaded)
- Primary promenade (step-free)
- Secondary paths
- Gateway entrance (×4)
- Accessible drop-off
- Bicycle parking

UNIVERSAL DESIGN

All primary routes step-free, max 1:20 gradient, tactile paving & rest nodes ≤ 60 m apart, high-contrast bilingual wayfinding, shaded seating along the loop, accessible WCs and an all-abilities playground — designed to national & international accessibility standards for People of Determination.

Direct step-free link to the Governmental Health Center gateway.